





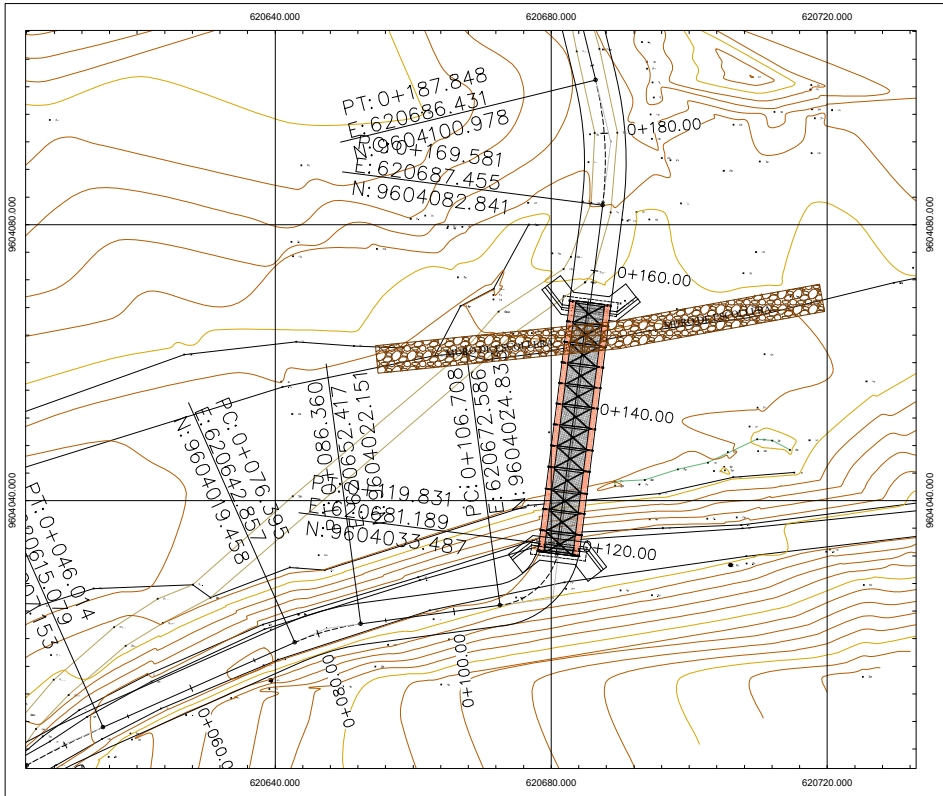

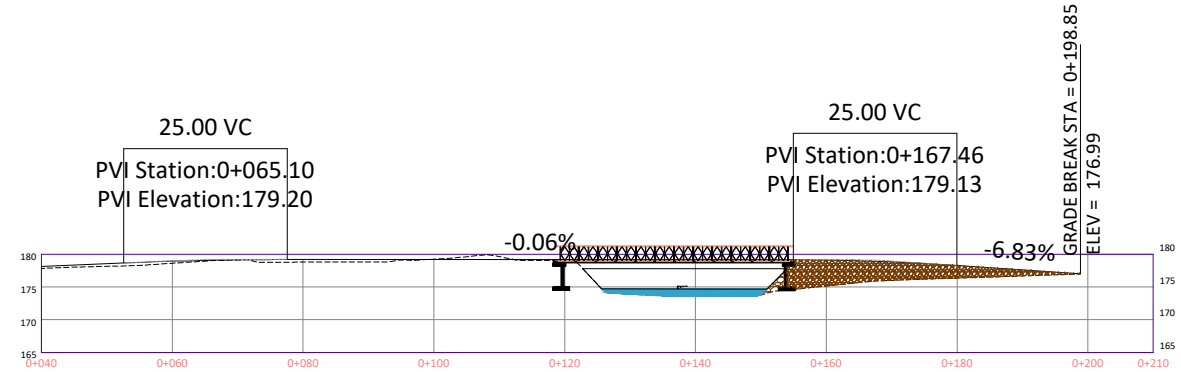

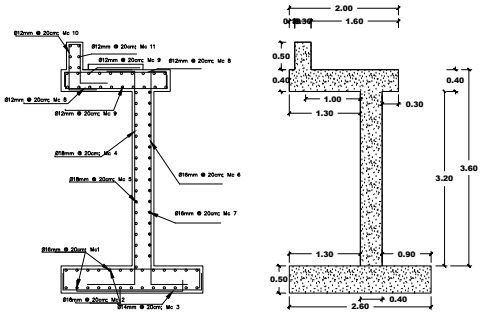


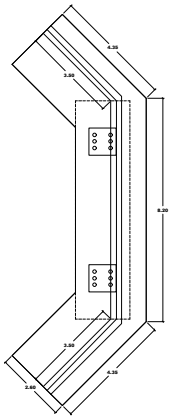


DETALLE DE BASE
ESCALA 1:50



DETALLE DE BASE
ESCALA 1:50

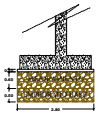

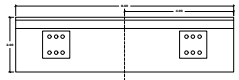


DETALLE DE BASE
ESCALA 1:50

DETALLE DE MURO ESTRIBO


ESCALA 1:50

DETALLE DE MURO DE ALA Y BASE
ESCALA 1:75

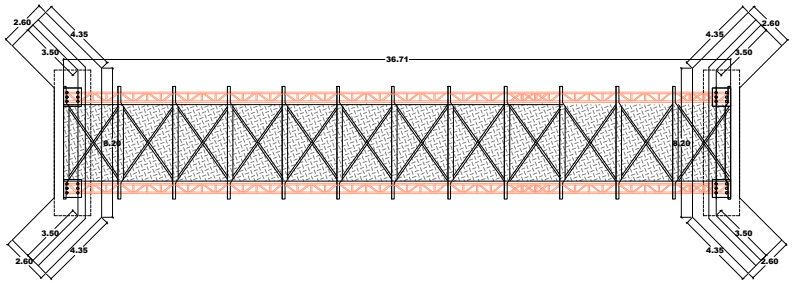

DETALLE PLANTA PUENTE BAILEY

ESCALA 1:150

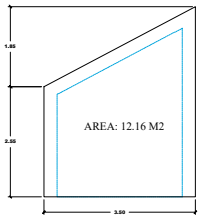


ESPECIFICACIONES TECNICAS


f'c = 240 Kg/cm2 : Resistencia a la compresión del Hormigón
fy = 4200 Kg/cm2 : Esfuerzo a la fluencia del refuerzo Longitudinal
Traslapes 40Ø, 60 cm escoger el mayor

Requisitos de Reglamentos para Concreto Estructural (ACI 318s-08) y Comentario


Acero estructural A.S.T.M. A-36
fy = 2540 kg/cm2 : Esfuerzo a la fluencia mínimo
Fu = 4060 kg/cm2 : Resistencia
Specification for the design of cold-formed steel structural members AISI
Soldadura E6011,E6013

TIPO DE HIERROS

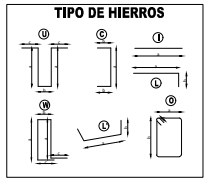


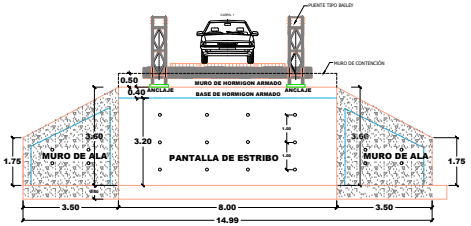


VISTA FRONTAL DEL ESTRIBO
ESCALA 1:75

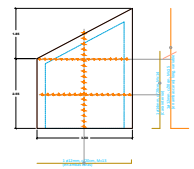

SECCION LONGITUDINAL DEL ALA TIPO 1
ESCALA 1:50

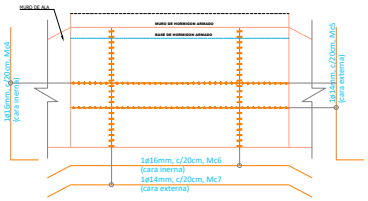

DETALLE PANTALLA DE MURO
ESCALA 1:75

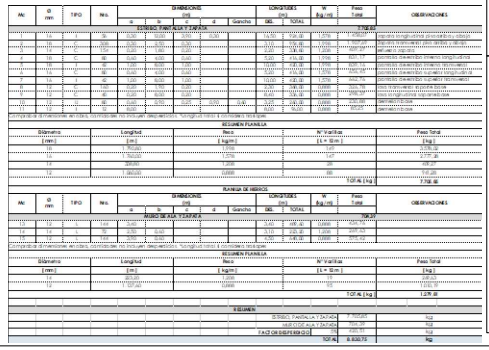

GOBIERNO AUTONOMO DESCENTRALIZADO PROVINCIAL DE EL ORO
Ing. Clemente Bravo Riofrio
PREFECTO
ADMINISTRACION 2023-2027

EL ORO PREFECTURA

DIRECCION ESTUD, PROY Y COOPERACION.

UBICACIÓN:
CANTON SANTA ROSA, PARROQUIA TORATA

PROYECTO:
"CONSTRUCIÓN DE ESTRIBOS PARA COLOCACION DE PUENTE BAILEY EN EL SITIO EL PLAYON PARROQUIA TORATA, CANTON SANTA ROSA, PROVINCIA DE EL ORO."

CONTIENE:
LEVANTAMIENTO PLANIMETRICO, PERFIL DEL TERRENO,SECCION LOGITUDINAL DEL MUROO DE ALA TIPO 1, DETALLE PANTALLA DE MURO, DETALLE PLANTA PUENTE BAILEY,VISTA FRONTAL DEL ESTRIBO, DETALLE DE MURO ESTRIBO,DETALLE PUENTE BASE,DETALLE ANCLAJE.

LAMINAS: 1 / 1
ESCALAS: INDICADAS
ELABORADO: W.M.T.O
FECHA: FEBRERO- 2026
REVISADO: Ing. JAIME ORTEGA CARRILLO JEFE DE ESTUDIOS, PROY. Y COOP.
APROBADO: Ing. WILMER TORO OCHOA. DIREC. DE ESTUDIOS, PROY. Y COOP.